
PRZEKRÓJ A-A

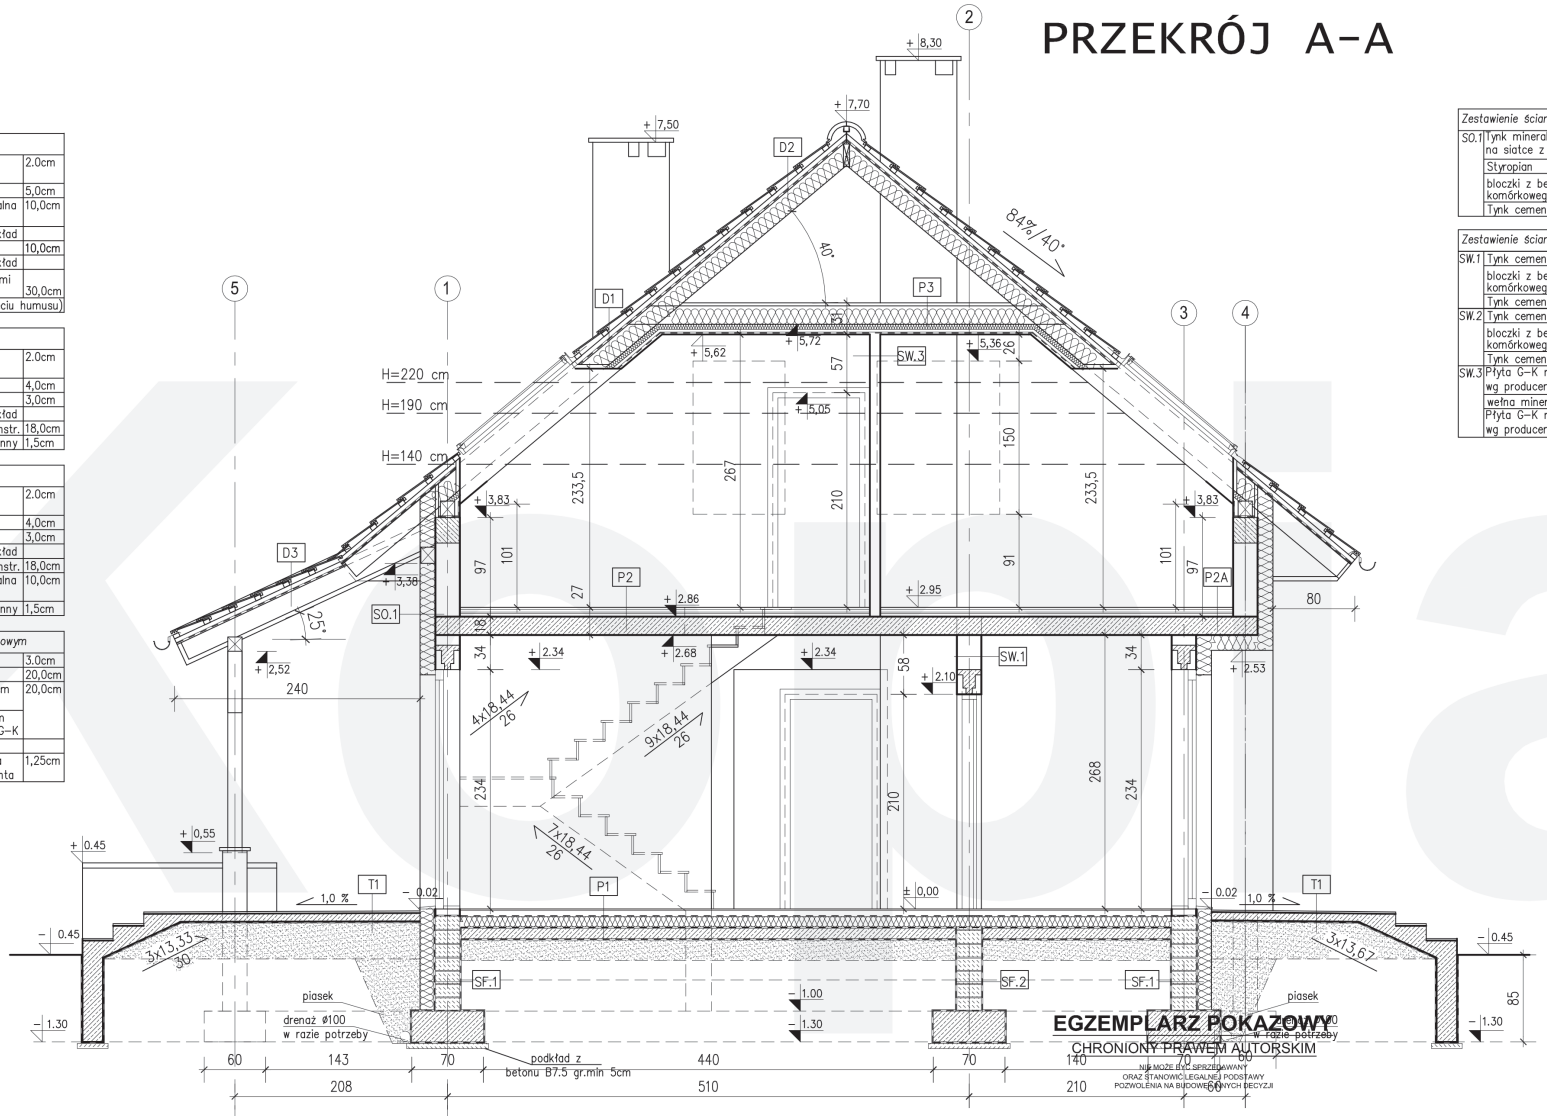

EGZEMPLARZ POKAZOWY
CHRONIONY PRAWEM AUTORSKIM
NIE MOŻE BYĆ SPRZEDAWANY
ORAZ STANOWIĆ LEGALNEJ PODSTAWY
POZWOLENIA NA BUDOWĘ I INNYCH DECYZJI

Podłoga na gruncie – dom		
P.1	Płytki ceramiczne / panele podłogogowe	2.0cm
	Gładź cementowa	5,0cm
	Styropian/wełna mineralna twarda	10,0cm
	folia PE klejona na zakład	
	Beton B 25	10,0cm
	folia PE klejona na zakład	
	Piasek ubijany warstwami na mokro	30,0cm
	grunt rodzimy (po zdjęciu humusu)	

Strop nad parterem		
P.2	Płytki ceramiczne / panele podłogogowe	2.0cm
	Gładź cementowa	4,0cm
	Styropian	3,0cm
	folia PE klejona na zakład	
	Strop żelbetowy wg konstr.	18,0cm
	Tynk cementowo-wapienny	1,5cm

Strop nad podcieniem		
P.2A	Płytki ceramiczne / panele podłogogowe	2.0cm
	Gładź cementowa	4,0cm
	Styropian	3,0cm
	folia PE klejona na zakład	
	Strop żelbetowy wg konstr.	18,0cm
	Styropian/wełna mineralna twarda	10,0cm
	Tynk cementowo-wapienny	1,5cm

Strop nad poddaszem użytkowym		
P.3	Deski podłogowe	3.0cm
	Jętki	20,0cm
	Wełna mineralna gr.15cm między jętkami	20,0cm
	Wełna mineralna gr.5cm między rusztem płyty G-K	
	Folia paroizolacyjna	
	Płyta G-K podwieszana na ruszcie wg producenta	1,25cm

Zestawienie ścian zewnętrznych		
SO.1	Tynk mineralny na siatce z włókna szklan.	1,2cm
	Styropian	15,0cm
	bloczki z betonu komórkowego odm.600	24,0cm
	Tynk cementowo-wapienny	1,5cm

Zestawienie ścian wewnętrznych		
SW.1	Tynk cementowo-wapienny	1,5cm
	bloczki z betonu komórkowego odm.600	24,0cm
	Tynk cementowo-wapienny	1,5cm
SW.2	Tynk cementowo-wapienny	1,5cm
	bloczki z betonu komórkowego odm.600	12,0cm
	Tynk cementowo-wapienny	1,5cm
SW.3	Płyta G-K na ruszcie wg producenta	1,5cm
	wełna mineralna	7,0cm
	Płyta G-K na ruszcie wg producenta	1,5cm

Dach nad poddaszem uzytkowym		
D.1	Dachówka cementowa	3.0cm
	Łaty	4x6cm
	Kontrłaty	3x5cm
	Folia FWK wstępnego krycia o paroprzepuszcz. >1000g/m2/24h	
	Wełna mineralna gr.15cm między krokwiami	20,0cm
	Wełna mineralna gr.5cm między rusztem płyty G-K	
	Folia paroizolacyjna	
	Płyta G-K na ruszcie wg producenta	1,25cm

Ściany fundamentowe		
SF.2	Izolacja wodochr. – preparat bitumiczny	
	bloczki betonowe B20	24,0cm
	prep. bitumiczny	

Dach nad poddaszem nieużytkowym		
D.2	Dachówka cementowa	3.0cm
	Łaty	4x6cm
	Kontrłaty	3x5cm
	Folia FWK wstępnego krycia o paroprzepuszcz. >1000g/m2/24h	
	Wełna mineralna między krokwiami	15,0cm
	Płyta G-K na ruszcie wg producenta	1,25cm

Ściany fundamentowe		
SF.1	Zaprawa klejowa na siatce	
	Stropian ekstrudowany	15,0cm
	Izolacja wodochr. – preparat bitumiczny	
	bloczki betonowe B20	24,0cm
	prep. bitumiczny	

Dach nieocieplany		
D.3	Dachówka cementowa	3.0cm
	Łaty	4x6cm
	Kontrłaty	3x5cm
	Folia FWK wstępnego krycia o paroprzepuszcz. >1000g/m2/24h	
	Pustka między krokwiami	20,0cm
	Podbitka z desek	2,0cm

Taras na gruncie		
T.1	Płytki gresowe mrozoodp. na zaprawie elastycznej połączonej z izol. ściany za pomocą taśmy uszczel.	1,5cm
	Płyta żelbetowa ze spadkiem 1,0%	8,0cm
	Piasek ubijany warstwami na mokro	30,0cm
	grunt rodzimy (po zdjęciu humusu)	

Niniejszy projekt jest wersją demonstracyjną projektu gotowego autorstwa pracowni projektowej ARCHIPORTAL. Jest on chroniony na mocy przepisów zawartych w ustawie o prawie autorskim i prawach pokrewnych z dnia 04.02.1994 (Dz. Ustaw nr 24 poz. 83 z dnia 23.02.1994 z późniejszymi zmianami). Wykorzystanie tego projektu do celów handlowych, dalszej odsprzedaży, reprodukowania, kopiowania w całości czy też częściowo bez wiedzy i zgody pracowni projektowej ARCHIPORTAL jest zabronione.